
SEMISÓTANO | TOMACORRIENTES

PROPUESTA DE UBICACIÓN · REVISIÓN 01

Arquitectura A01 + cuadro de cantidades del usuario

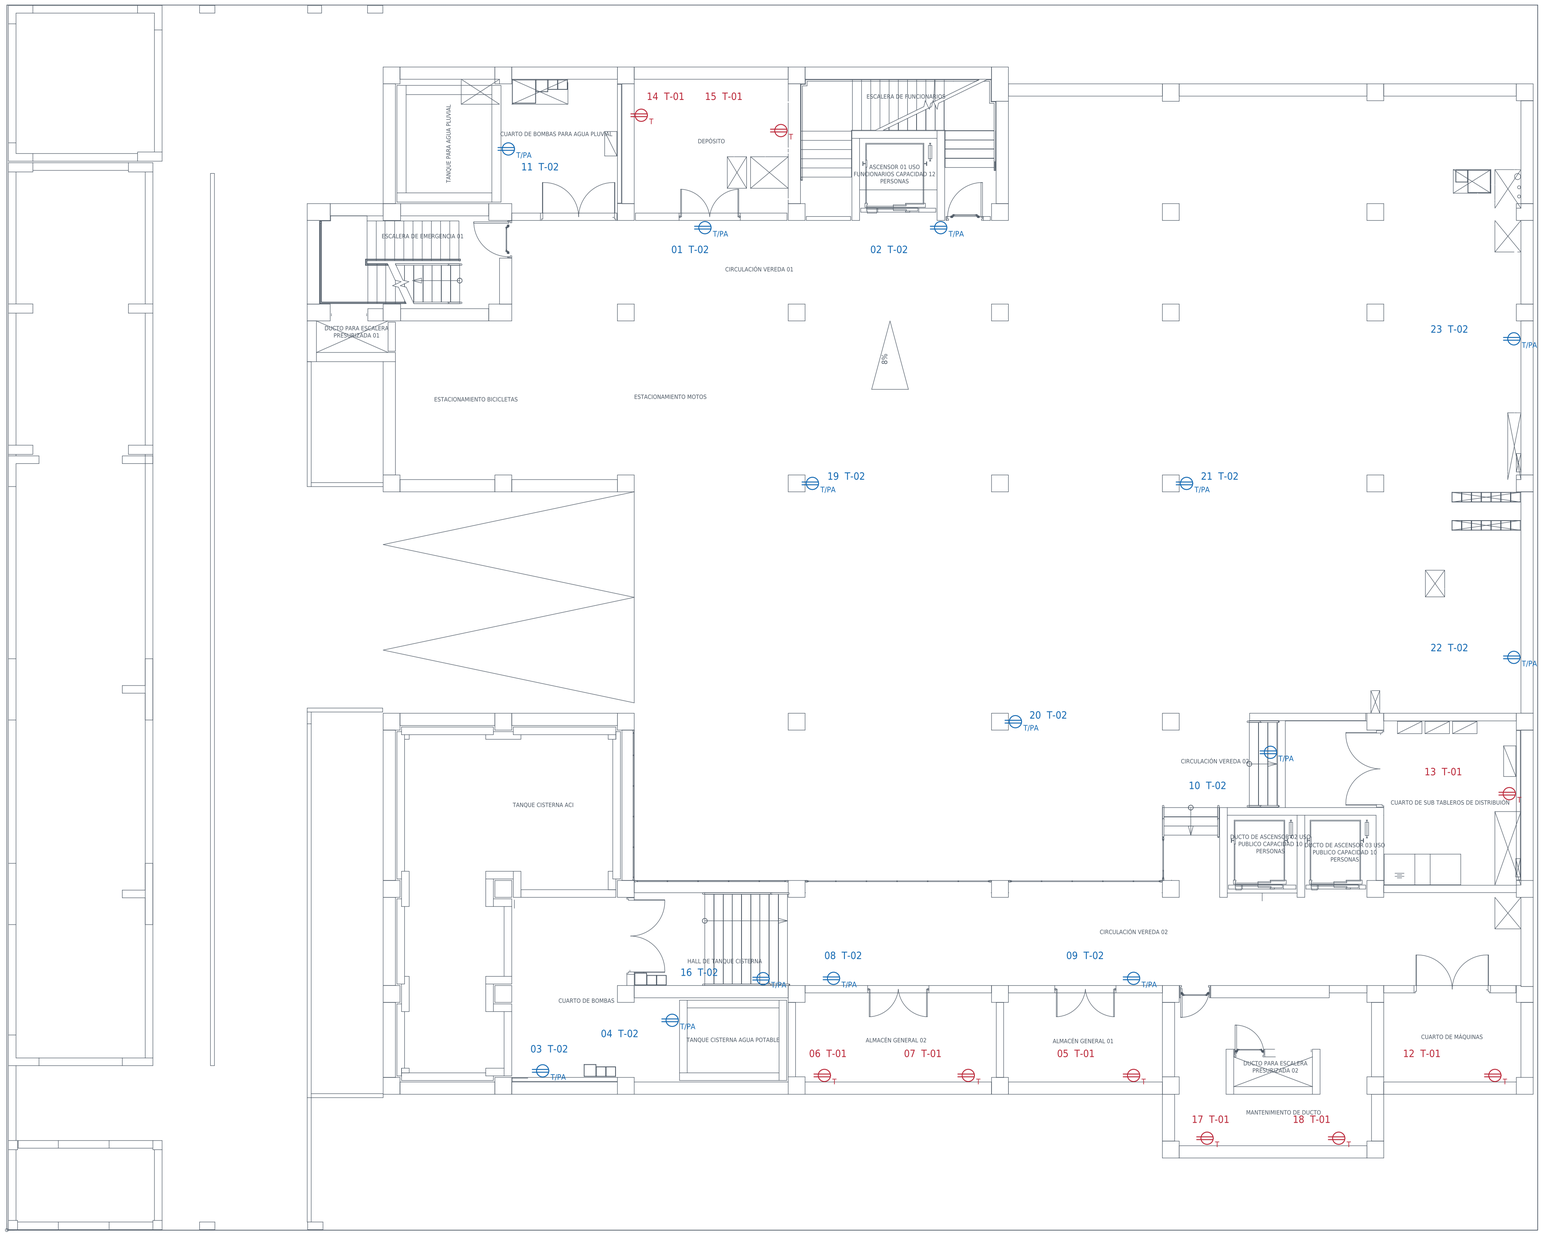

23 PUNTOS DOBLES

9 de muro + 14 estancos

SIMBOLOGÍA

T — T-01 · Doble 2P+T en muro
+0.40 m sobre NPT · 9 puntos

T/PA — T-02 · Doble 2P+T estanco
+1.10 m sobre NPT · 14 puntos

RELACIÓN DE UBICACIONES

01 / 02	Vereda 01
03 / 04	Cuarto de bombas
05	Almacén general 01
06 / 07	Almacén general 02
08 / 09 / 10	Vereda 02
11	Bombas de agua pluvial
12	Cuarto de máquinas
13	Cuarto de subtableros
14 / 15	Depósito
16	Hall de tanque cisterna
17 / 18	Mantenimiento de ducto
19 / 20 / 21	Circulación vehicular central
22 / 23	Circulación vehicular lateral

LECTURA DEL PLANO

Cada símbolo representa un punto doble.
El número identifica su registro; T-01/T-02 indica el tipo.
Alturas referidas al nivel de piso terminado (NPT).

ALCANCE DE ESTA REVISIÓN

Ubicaciones propuestas para revisión sobre arquitectura.
Los sectores central y lateral se interpretan por geometría.
Circuitos del Excel guardados en atributos editables.
Sin circuitos trazados ni canalizaciones.

DISTRIBUCIÓN DE PUNTOS · PARA REVISIÓN

Modelo en metros · Escala de la ventana 1:100 en hoja A1 (841 × 594 mm) · SS-01

Base gráfica DGE 09-93-17; PA según 09-93-19. Cantidades y alturas: Excel recibido.