SEMISÓTANO | LUMINARIAS INTEGRADAS

Distribución de luminarias para revisión visual · Sin recorridos



162 LUMINARIAS

2.931 W · 5 tipos utilizados

LEYENDA

L-01 · 20 unidades
Lineal larga LED · 36 W

L-01-15 · 118 unidades
Lineal corta LED · 15W-A

L-02 · 13 unidades
Aplique circular · 20 W

L-04B · 7 unidades
Downlight empotrado · 11 W

L-03-IP65 · 4 unidades
Panel hermético · 26 W

LECTURA

Los símbolos en planta no llevan códigos exteriores. Tipo, altura, ambiente y fuente quedan como atributos editables.

POSICIONES

Coordenadas y alturas de la memoria DIALux REV1. Se conserva la unidad individual de Vereda 02 (pág. 118).

ALCANCE


Dibujo en planta XY. Las alturas se guardan como datos. El tamaño del símbolo es gráfico; no es la huella física del equipo.

Escala 1:100 · Modelo en metros · Fuente: arquitectura y memoria del usuario

Bloques según propuesta gráfica REV F · Cantidades y montaje sujetos a revisión del proyecto definitivo

SEMISÓTANO | DETALLE NORTE

Distribución de luminarias para revisión visual · Sin recorridos

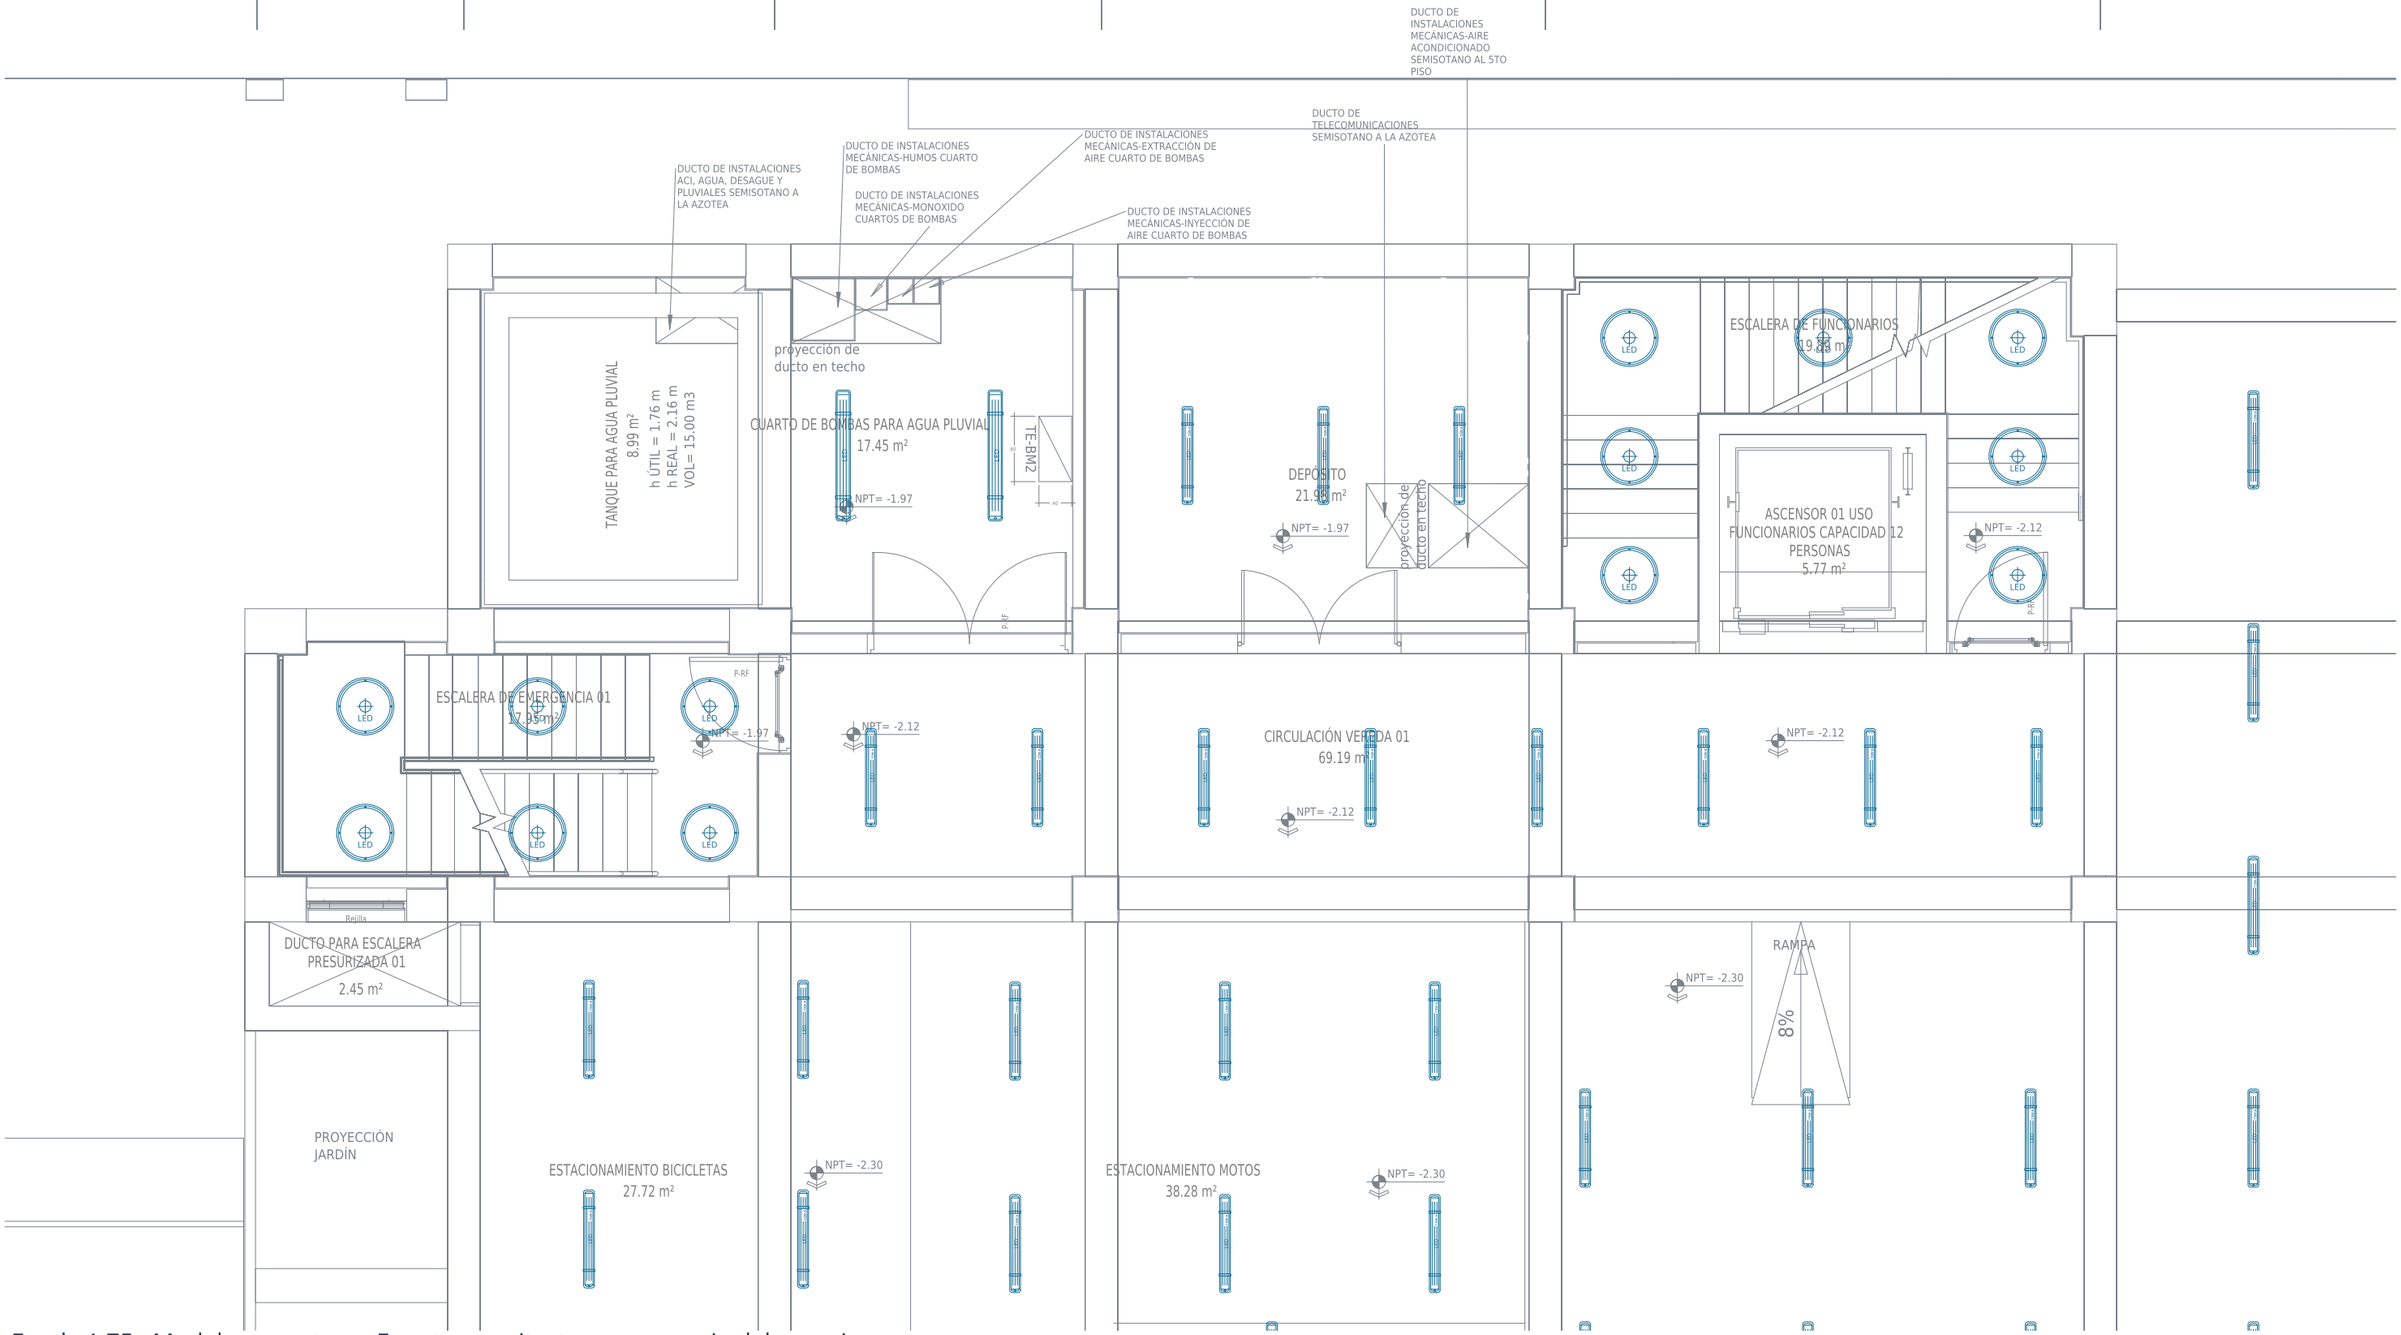


Escala 1:75 · Modelo en metros · Fuente: arquitectura y memoria del usuario

Bloques según propuesta gráfica REV F · Cantidades y montaje sujetos a revisión del proyecto definitivo

SEMISÓTANO | BOMBAS Y CISTERNAS

Distribución de luminarias para revisión visual · Sin recorridos

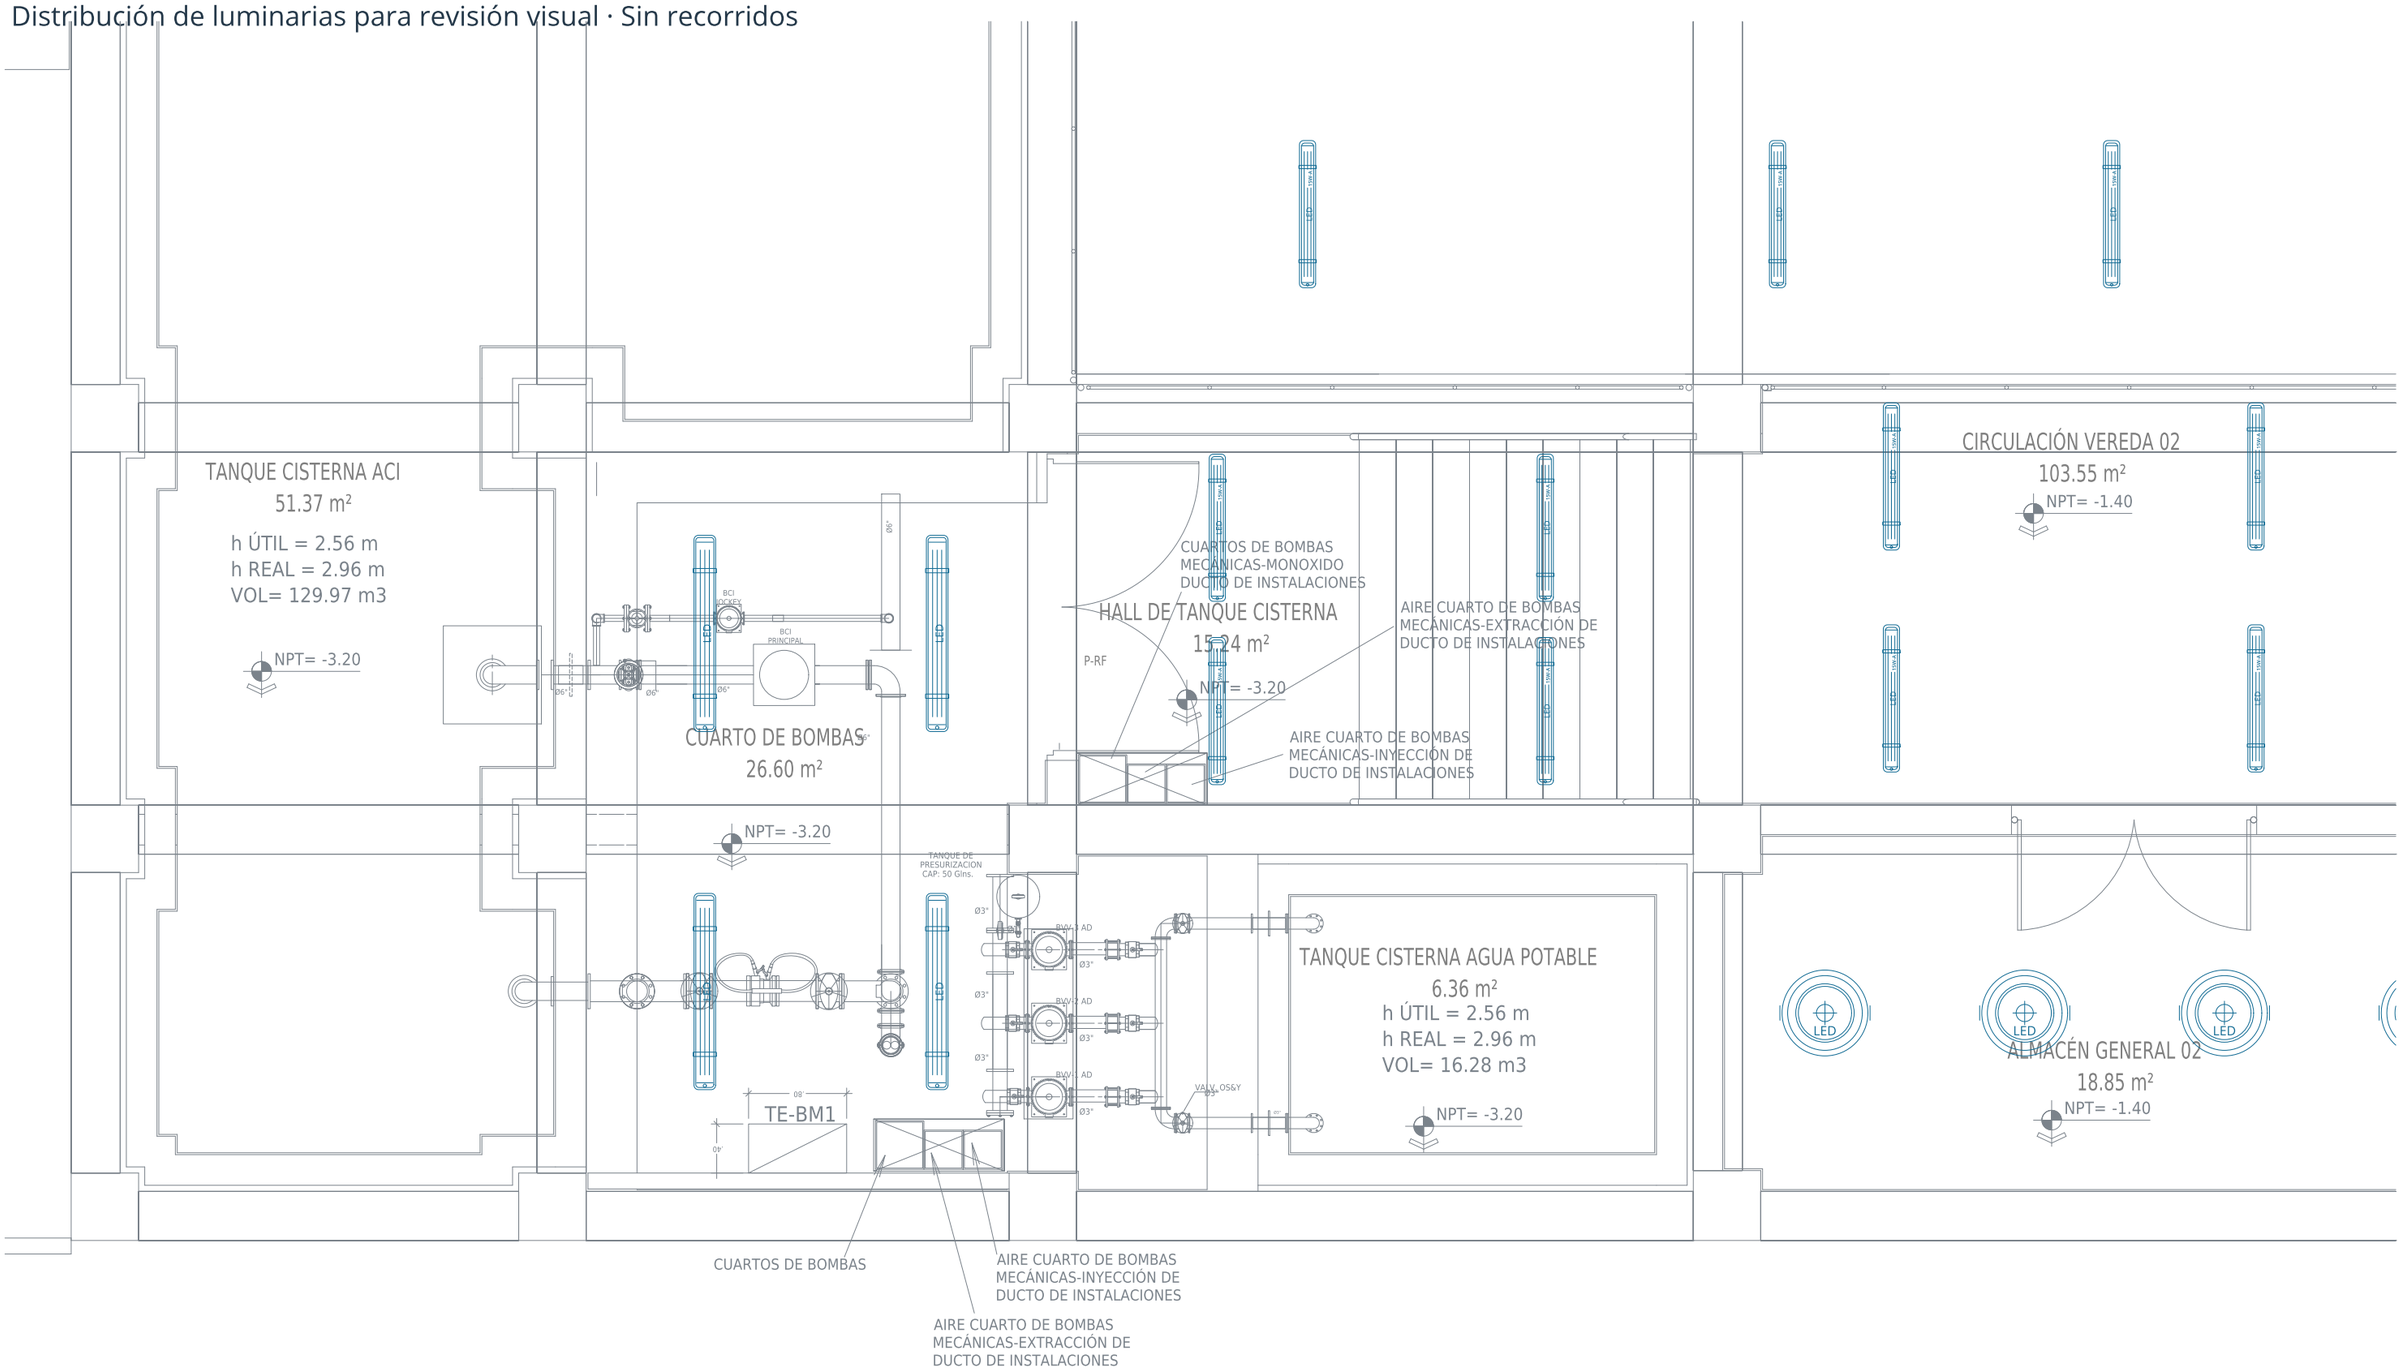


Escala 1:50 · Modelo en metros · Fuente: arquitectura y memoria del usuario

Bloques según propuesta gráfica REV F · Cantidades y montaje sujetos a revisión del proyecto definitivo

SEMISÓTANO | ALMACENES Y SERVICIOS

Distribución de luminarias para revisión visual · Sin recorridos

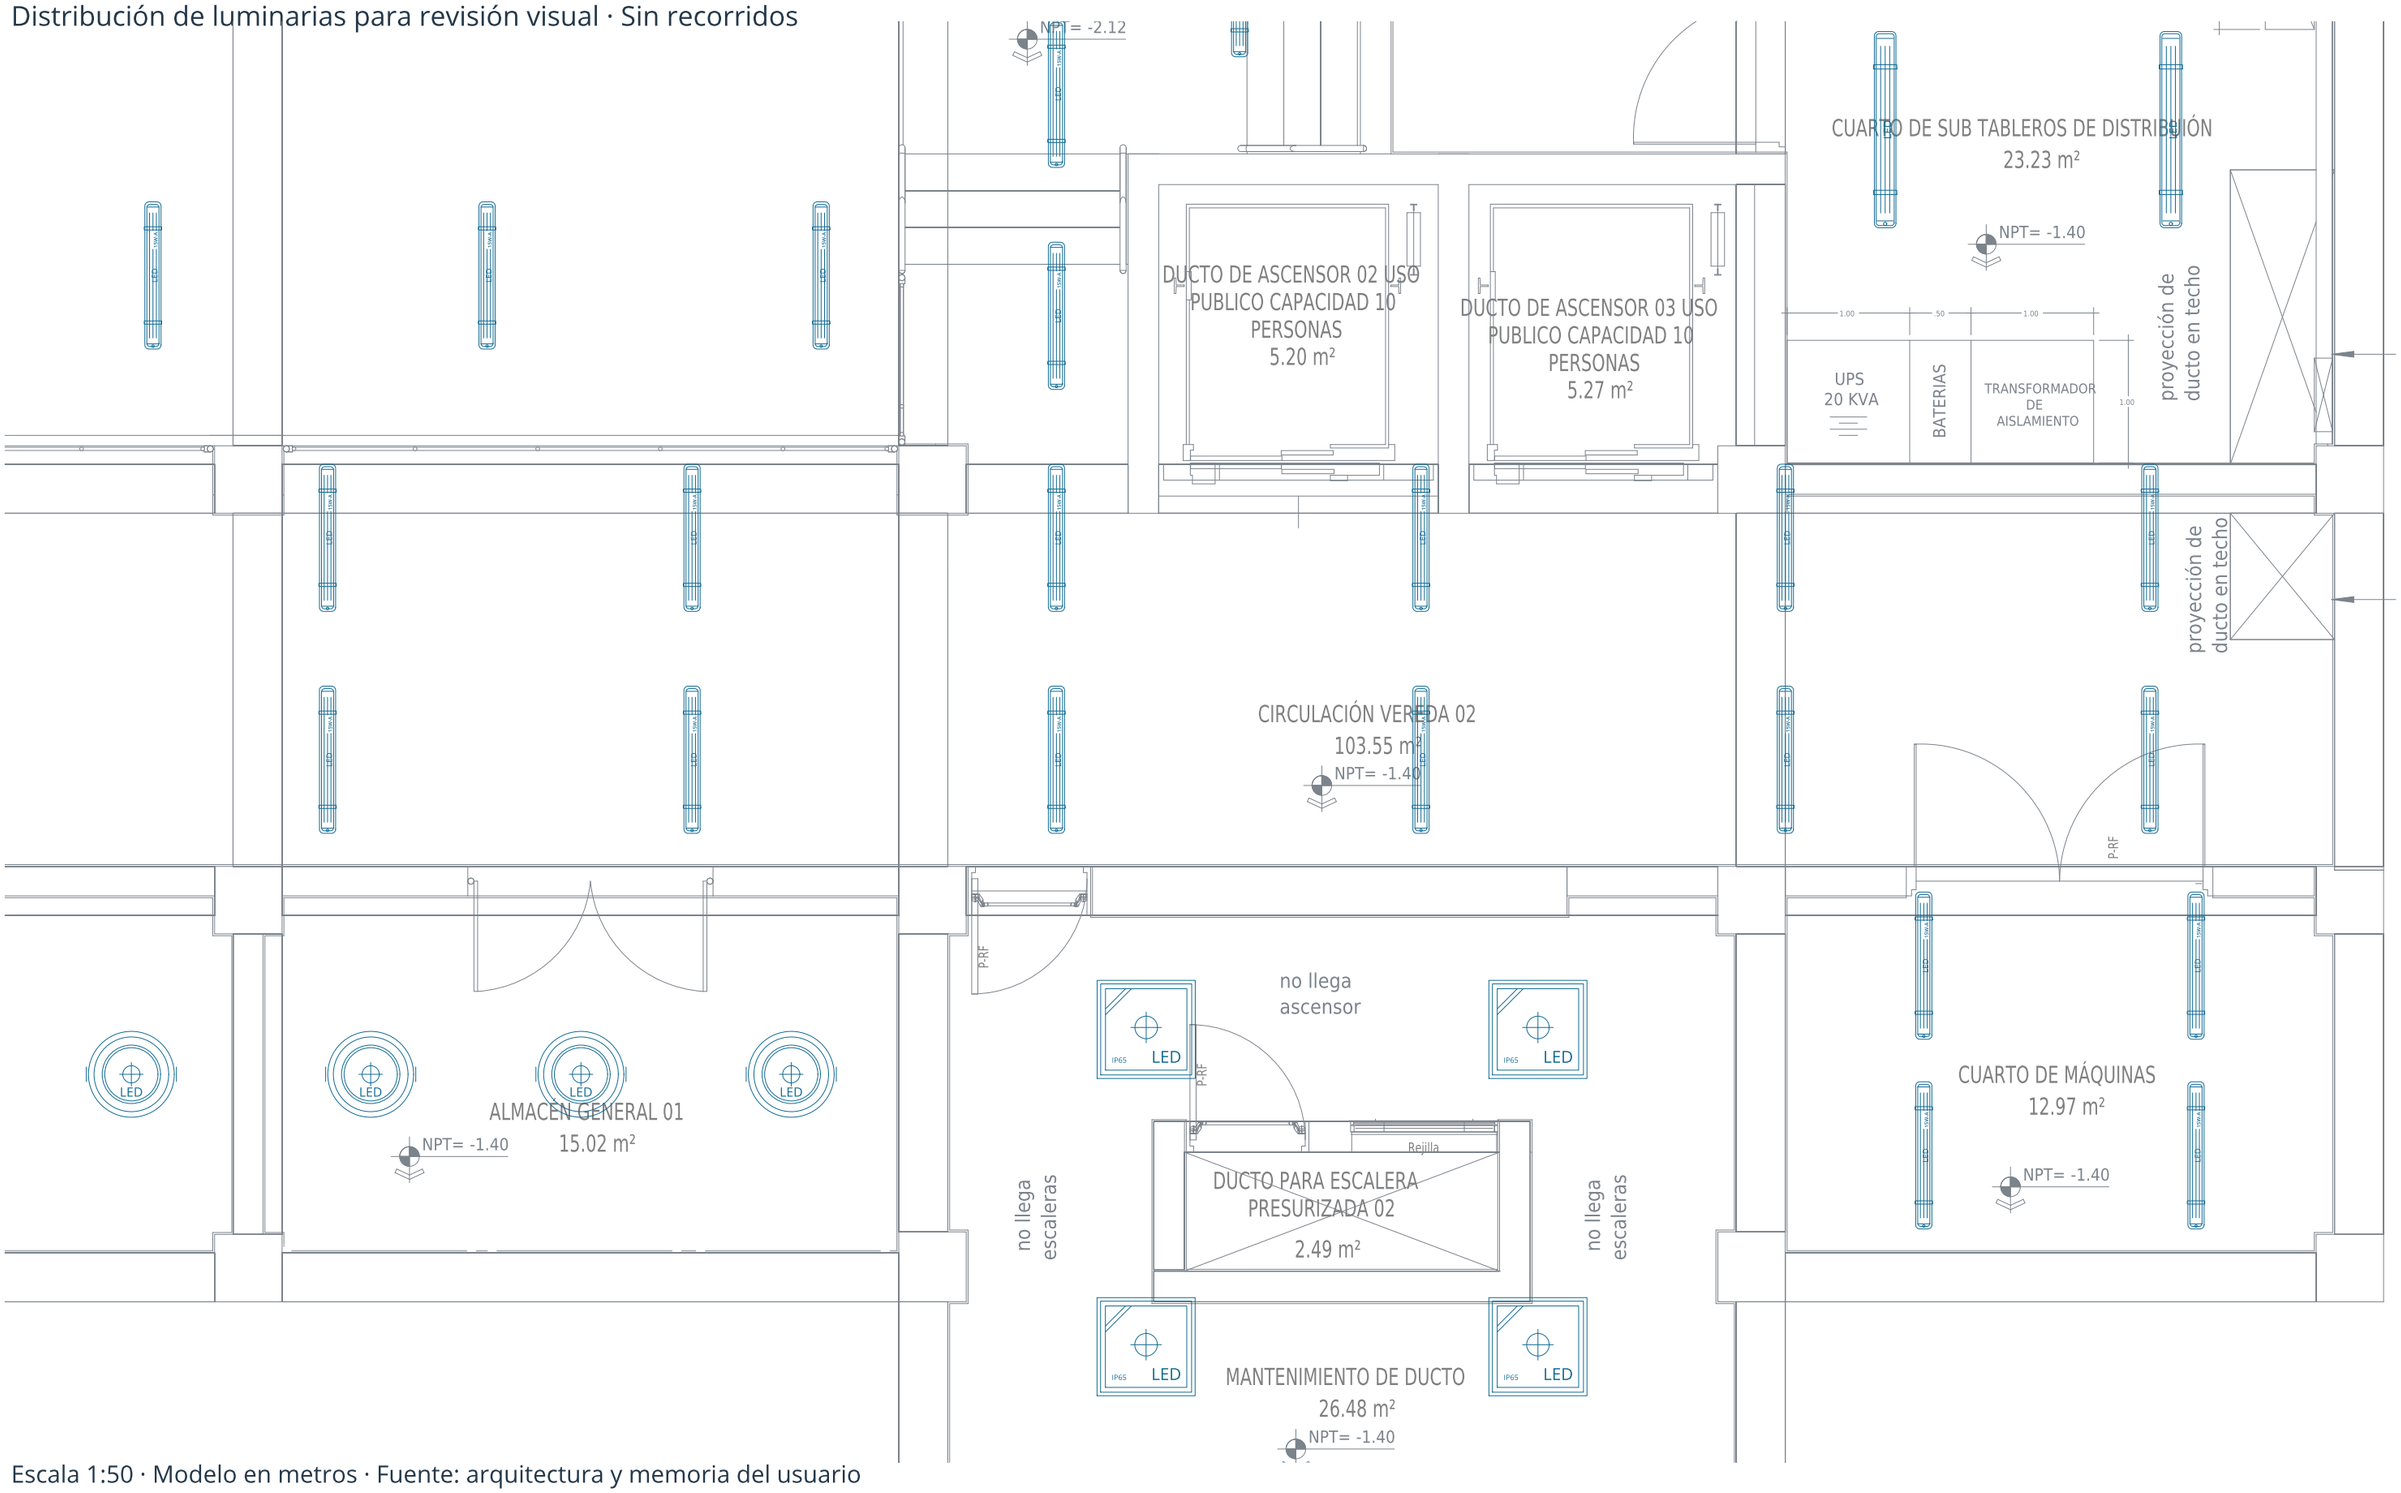

Escala 1:50 · Modelo en metros · Fuente: arquitectura y memoria del usuario

Bloques según propuesta gráfica REV F · Cantidades y montaje sujetos a revisión del proyecto definitivo